
경기형 학교시민교육 100인 토의 플로어플랜 v0.4 — 원탁 Ø1800


조원청사 신관 1층 로비 · 핑크 6 + 갈색 4 + 연두 2 = 원탁 12 · 의자 10석/원탁(120석) · 점선 원 = 착석 영역(테이블 끝+0.6m) · 도면 PL-001 축척 실측

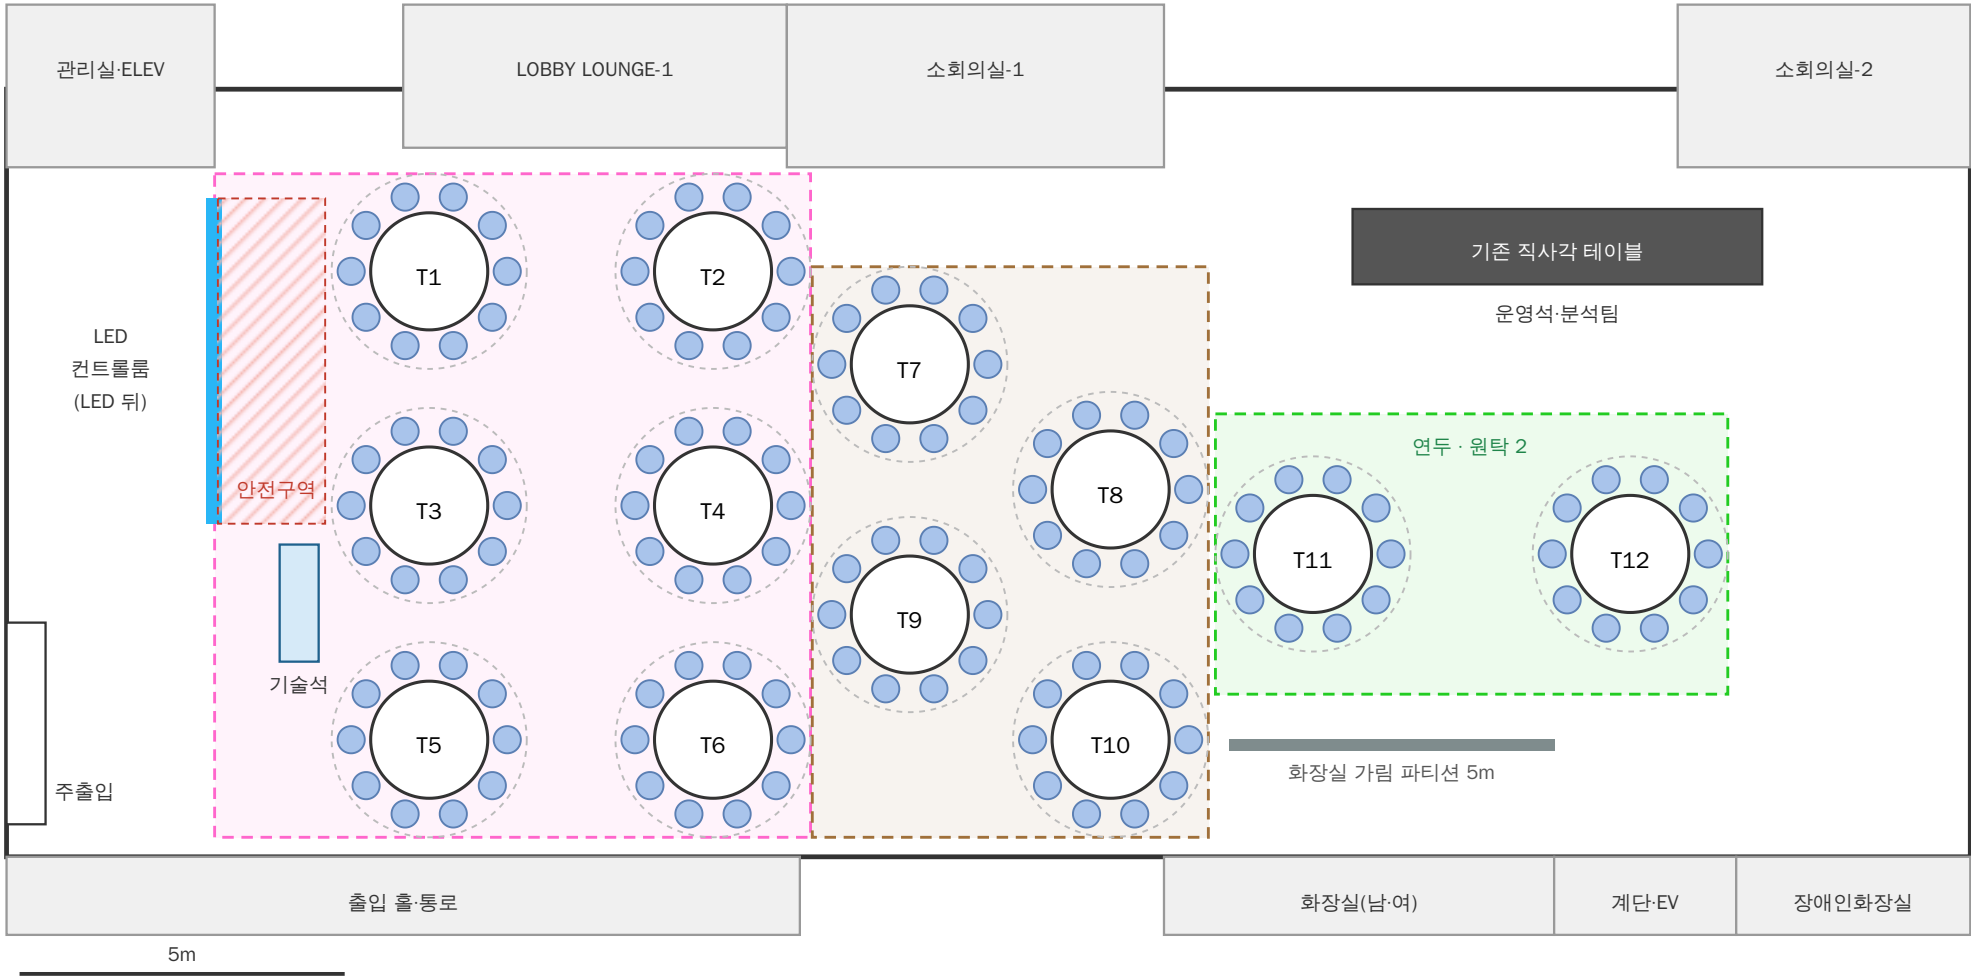

핑크 구역(점선) 원탁 6 · 갈색 구역 원탁 4(지그재그) · 연두 구역 원탁 2 · 하늘색 = LED · 빗금 = LED 앞 안전구역

경기형 학교시민교육 100인 토의 플로어플랜 v0.4 — 원탁 Ø1600

조원청사 신관 1층 로비 · 핑크 6 + 갈색 4 + 연두 2 = 원탁 12 · 의자 10석/원탁(120석) · 점선 원 = 착석 영역(테이블 끝+0.6m) · 도면 PL-001 축척 실측

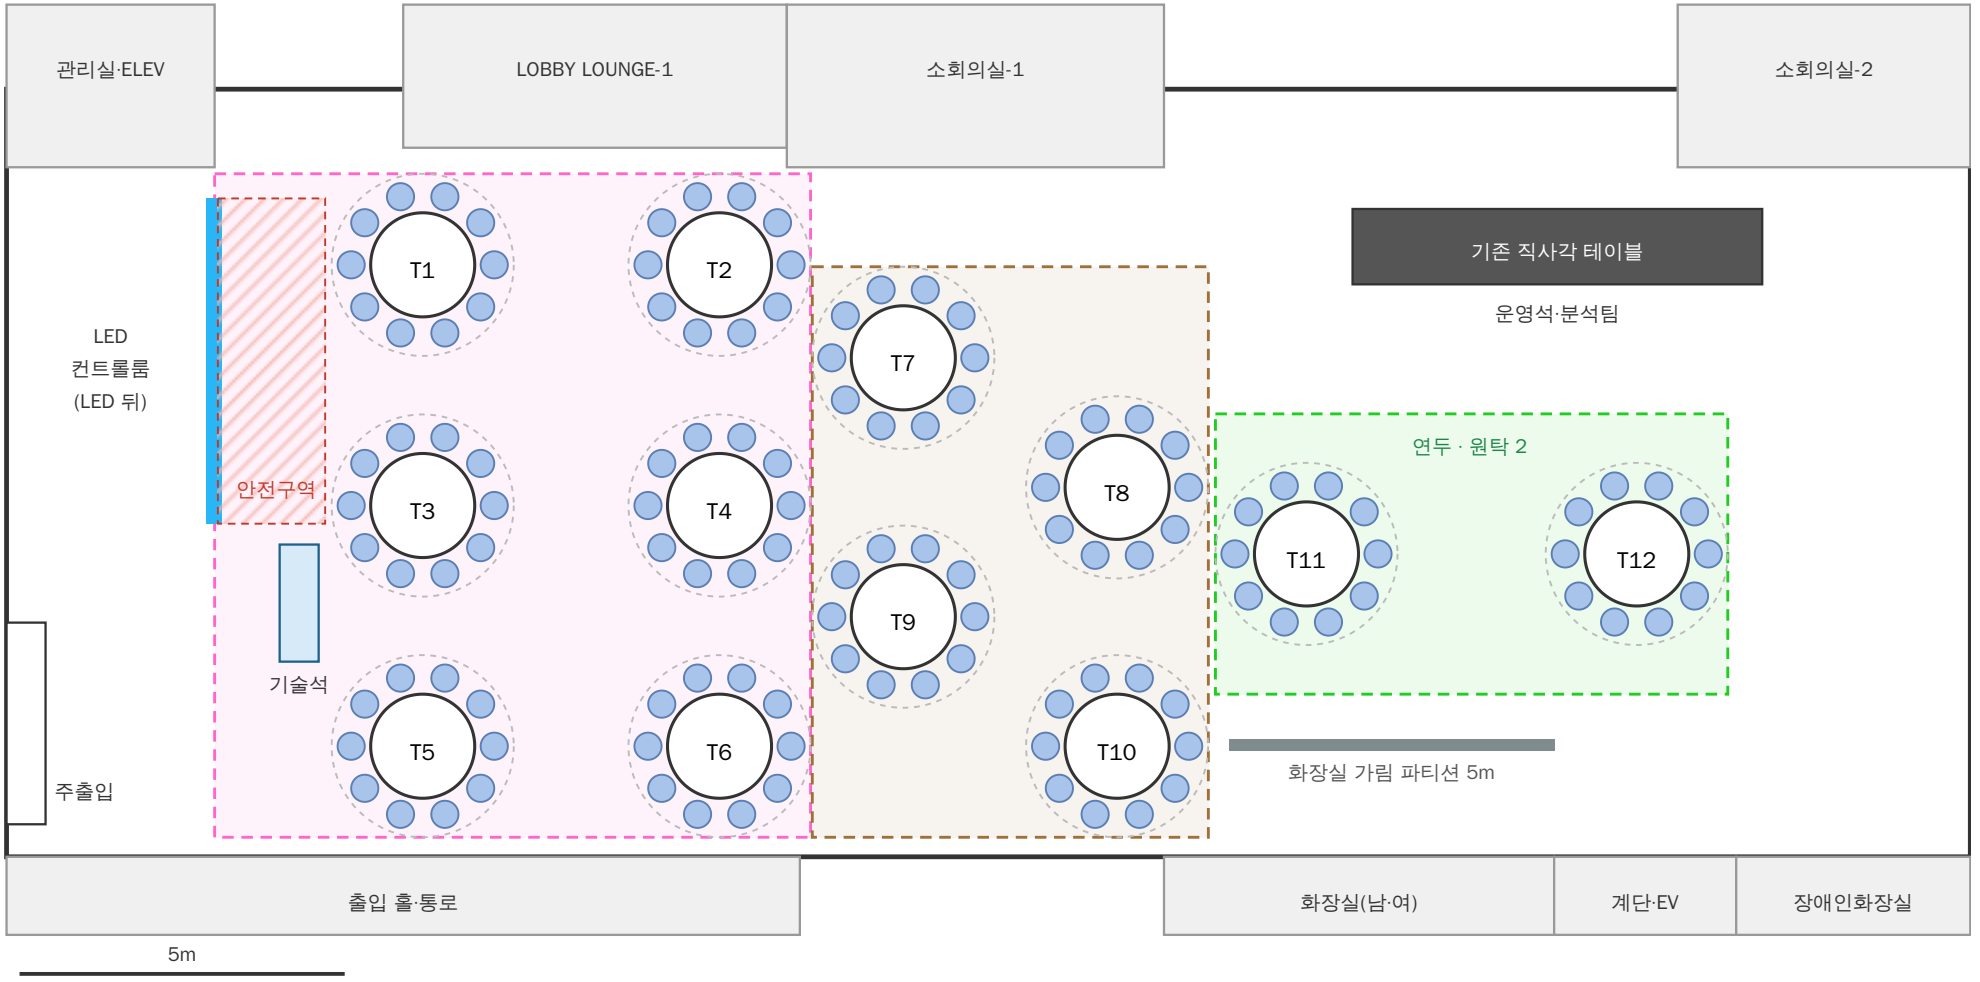

핑크 구역(점선) 원탁 6 · 갈색 구역 원탁 4(지그재그) · 연두 구역 원탁 2 · 하늘색 = LED · 빗금 = LED 앞 안전구역

원탁 모듈·통로 산출 (Ø1800 vs Ø1600)

의자 10석 기준 · 착석 영역 0.6m(의자+앉은 자세) · 권장 통로 0.9m(사람 통과), 최소 0.6m(옆걸음)

구분	Ø1800	Ø1600	산식
1인당 테이블 둘레(10석)	0.57m	0.50m	π×D÷10 (권장 0.6m 내외)
의자 간 중심 간격	0.75m	0.69m	2π×(D/2+0.3)÷10
착석 모듈 지름(원탁+의자)	3.0m	2.8m	D + 0.6×2
모듈+뒤 통로(권장 피치)	3.9m	3.7m	D + 0.6×2 + 통로 0.9
모듈 점유 면적(정사각 환산)	15.2㎡	13.7㎡	피치²

구역(실측 추정)	배치	방향	Ø1800 의자 등받이 간 통로	Ø1600 의자 등받이 간 통로
핑크 9.2×10.2m	2열×3행	동서(LED 앞 1.8m 제외)	1.36m · 충분	1.76m · 충분
		남북(행 사이)	0.60m · 최소(옆걸음)	0.90m · 충분
갈색 6.1×8.8m	2열 지그재그 4	대각 인접	0.64m · 최소(옆걸음)	1.05m · 충분
		같은 열	0.85m · 최소(옆걸음)	1.18m · 충분
연두 7.9×4.3m	1행×2	동서(원탁 사이)	1.88m · 충분	2.28m · 충분
		남북 여유(한쪽)	0.66m · 최소(옆걸음)	0.76m · 최소(옆걸음)

판단 — Ø1800은 핑크 구역 행 사이 통로가 0.60m로 최소 기준에 걸려 퍼실·투표기 회수 동선이 빡빡합니다. Ø1600은 핑크 0.90m로 권장(0.9m)을 맞추고, 갈색·연두도 모두 0.9m 이상입니다. Ø1600 권장(1인당 둘레 0.50m — 10석은 다소 촘촘, 참가자 8~9명+퍼실 1 착석 기준 무리 없음).

※ 구역 치수는 표시해 주신 범위를 도면(1/150, 5,900mm=112px)으로 환산한 추정치(±0.3m). 핑크 동서폭은 도면 치수 9,165 적용. 10/19 실측으로 확정

※ 기술석: LED 앞 남측에 직사각 1800×600 1개(LED 정면 시야 비켜 배치), LED 컨트롤룸은 LED 뒤 공간 사용 · 운영석·분석팀은 LOUNGE-2 기존 직사각 테이블 사용

※ 연두 구역 남측 화장실 앞 가림 파티션 약 5m · 원탁 의자 120석(참가자 100 + 퍼실 12 + 예비)