
경기형 학교시민교육 100인 토의 플로어플랜 (v0.3)

경기도교육청 조원청사 신관 1층 로비 · 원탁 13개(12+예비 1) · 테이블당 8명 · 신관 1층 도면(PL-001, 1/150) 기준 · 로비 약 35m×8.6m

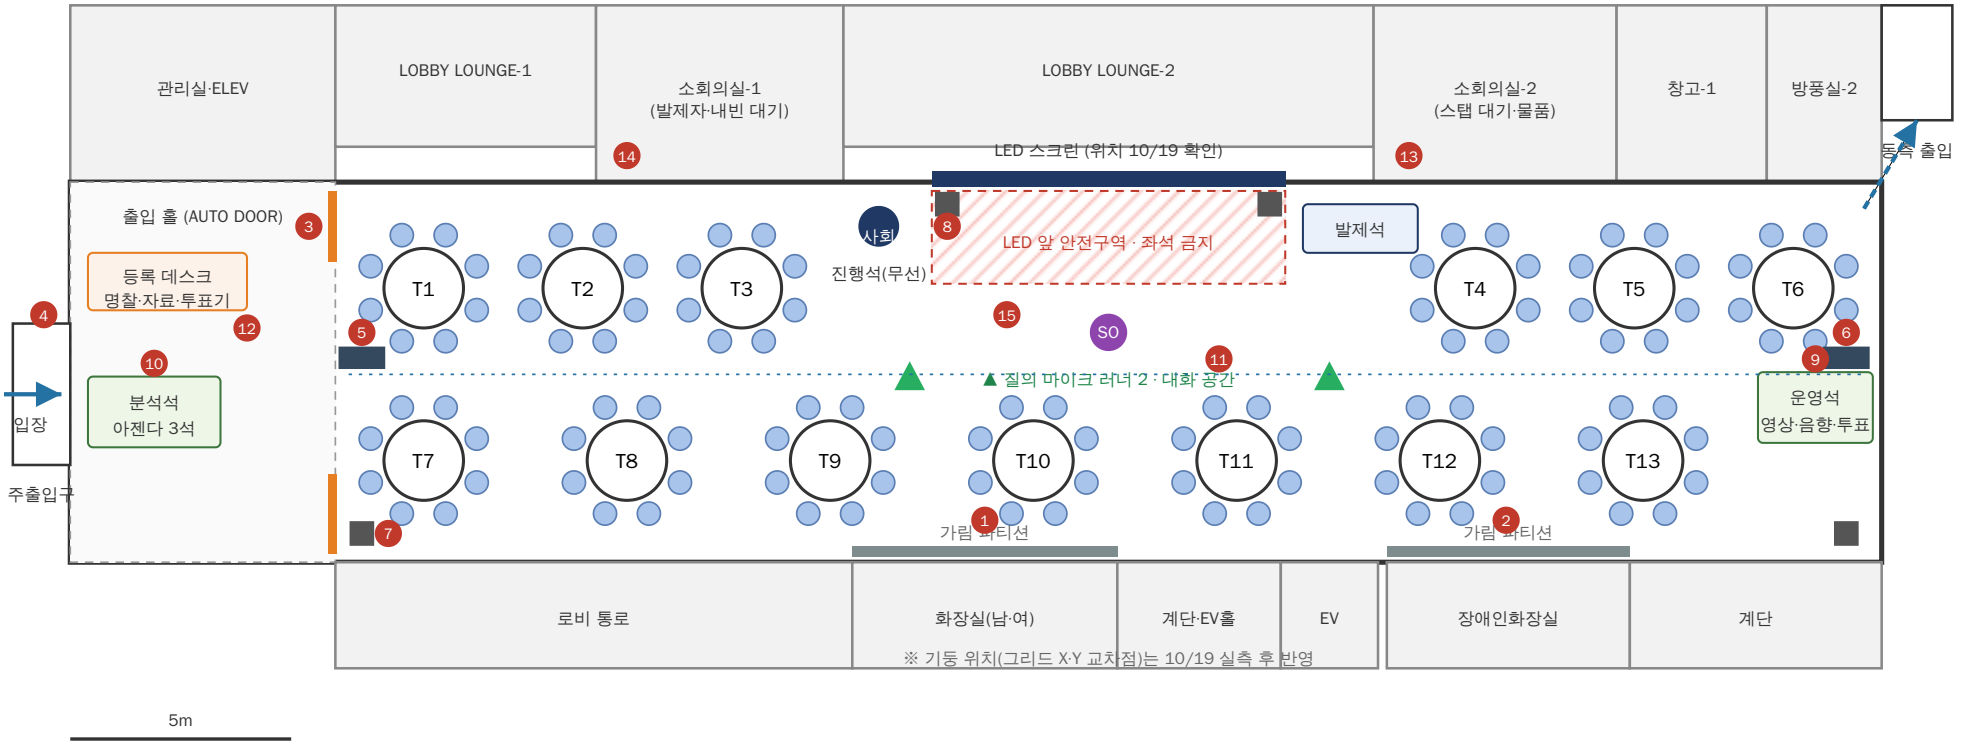

● 번호는 [표] 추가 준비물 번호 · ▬ 주황: 가림막 · ▬ 회색: 화장실 가림 파티션 · ■ 남색: 보조 모니터 · ■ 회색: 스피커 · → 입장(서측)·퇴장/비상(동측) · --- 중앙 통로(피난)

플로어플랜 배치 설명

v0.3 · 2026. 10. 13. · 코리아스픽스 숙의공론컨설팅본부

구분	배치	장비·인력
공간	신관 1층 로비(Y4~동측 벽 약 35m × 북측 회의실~남측 코어 약 8.6m). 서측 출입 홀(AUTO DOOR)·동측 방풍실 2곳 출입	도면 PL-001 기준 추정 치수
LED·대화 공간	북측 중앙(LOBBY LOUNGE-2 앞)에 LED 가정. 앞 안전구역은 비우고, 그 앞을 사회·발제·전체토의 대화 공간으로 사용	사회 무선 1 · 발제 유선 1·무선 1
원탁 13	북측 열 6개(대화 공간 좌우 3개씩) + 남측 열 7개. 테이블당 8명(12개 사용·1개 예비). 열 간 통로 약 1m	노트북·무선투표기 · 소그룹 퍼실
등록·분석	서측 출입 홀에 등록 데스크와 아젠다(분석)석. 등록 → 테이블 안내 → 착석, 입·퇴장 동선 분리	리셉션 · 아젠다 3석
운영석	동측 끝(T6 아래). 스크린 측면 시야, 동측 출입·창고와 가까워 장비 반입 용이	마마미디어 스위처·노트북 · 유선 LAN·공유기
부속 공간	소회의실-1: 발제자·내빈 대기 / 소회의실-2: 스탭 대기·물품 / 남측 화장실·장애인화장실 앞 가림 파티션	사용 허가 교육청 확인
음향	대화 공간 좌우 메인 스피커. 로비가 길어(35m) 동·서 끝 보조 스피커 필요 가능성	10/19 울림 점검

※ LED 실제 위치·크기, 기둥, 콘센트·랜 포트, 로비 라운지 가구 이동 가능 여부는 10/19(월) 10:00 마마미디어 동행 답사에서 확인 후 v0.4 반영

※ 남측 열과 코어(화장실·EV) 사이 통로 폭 확보 필요 — 실측 결과에 따라 원탁 지름(1.8m) 또는 열 배치 조정

※ 로비가 길어 양 끝 테이블(T1·T6·T7·T13)에서 스크린 거리 약 15m — 보조 모니터 필요 여부 검토

추가 준비물·설치 계획

실행계획서 v0.5.24 「공론장 조성」·10/8 현장 미팅 기준 · 수량은 안(案), 10/19 답사 후 확정

No	항목	위치·기준	수량(안)	담당
1·2	화장실 가림 파티션	남측 화장실(약 6m)·장애인화장실(약 5.5m) 앞. 출입구는 열어 두고 시선만 차단. 시설물 고정·훼손 방지(자립형)	2구간 · 패널 약 7개	렌탈 업체 / 설치 허용 방식 교육청 확인
3	출입 통제 가림막·임시 벽체	서측 출입 홀↔로비 경계. 등록 전 입장 통제, 외부 통행 시선 차단	2구간	렌탈 업체
4	안내 표지(X배너)	주출입구·등록·화장실·동측 출입. 「100인 토의」 행사 안내 및 동선 표시	4개	코리아스픽스 제작
12	테이블 배치도 보드	등록 데스크 옆. 배정 테이블 번호 확인용	1개	코리아스픽스 제작
5·6	보조 모니터(스탠드형)	로비 양 끝(T1·T7, T6·T13 쪽). 스크린까지 약 15m 떨어진 테이블 시야 보완	2대 + 분배기	마마미디어 / 필요 여부 10/19 판단
7	보조 스피커	로비 양 끝 남측. 35m 긴 공간·울림 대비	2대	음향 업체
8	메인 스피커·마이크	대화 공간 좌우. 무선 4(사회·발제·러너 2)+유선 1	스피커 2 · 마이크 5	음향 업체
9	운영·집계 데스크	동측 끝. 스위처·노트북·무선투표 수신기, 투표기 충전·보관, 종이 대체 응답지 보관	테이블 2 · 의자 4	마마미디어 / 비품 교육청
10	분석석·기록 회수 위치	서측 출입 홀. 테이블 기록지 회수함, 분석 노트북 3	테이블 2 · 의자 3	코리아스픽스
11	통신(폐쇄형 공유기·유선 LAN)	로비 중앙 + 양 끝 분산(13개 테이블 노트북 접속). 랜 포트 위치 확인	공유기 3 · LAN 케이블	마마미디어 / 접속 정책 교육청
—	전원·케이블 정리	테이블 노트북 13·운영 장비 전원. 통로 횡단 케이블은 덮개(몰딩) 처리	멀티탭·릴선 15 · 케이블 덮개	마마미디어
13	스탭 대기·물품 보관	소회의실-2. 자료집·예비 출력물·기록지·필기구 보관, 잔여물 회수	—	사용 허가 교육청 확인
14	발제자·내빈 대기	소회의실-1. 교육감 참석 시 의전 동선	—	사용 허가 교육청 확인
15	기념촬영 위치	폐회 단체사진 — LED 앞 대화 공간(안전구역 밖)	—	코리아스픽스
—	원탁·의자	원탁 13(지름 약 1.8m) · 의자 104 + 진행·스탭용	원탁 13 · 의자 약 120	렌탈 업체 / 교육청 보유분 확인
—	테이블 비품	테이블 번호 표지 13, 명찰 100+스탭, 자료집 110, 기록지, 필기구, 무선투표기 110(예비 10), 종이 대체 응답지 110	—	코리아스픽스

※ 공통: 시설물 고정 시 바닥·벽 훼손 금지(테이프 사용 범위 교육청 확인), 행사 후 원상복구

※ 10/28(수) 오후 설치·전체 리허설 — 반입 시간·주차(주차관리 매뉴얼)·하역 동선 교육청과 확정

※ 피난 동선: 원탁 열 사이 중앙 통로와 양측 출입구까지 통로 폭 확보, 비상구 위치 10/19 확인